


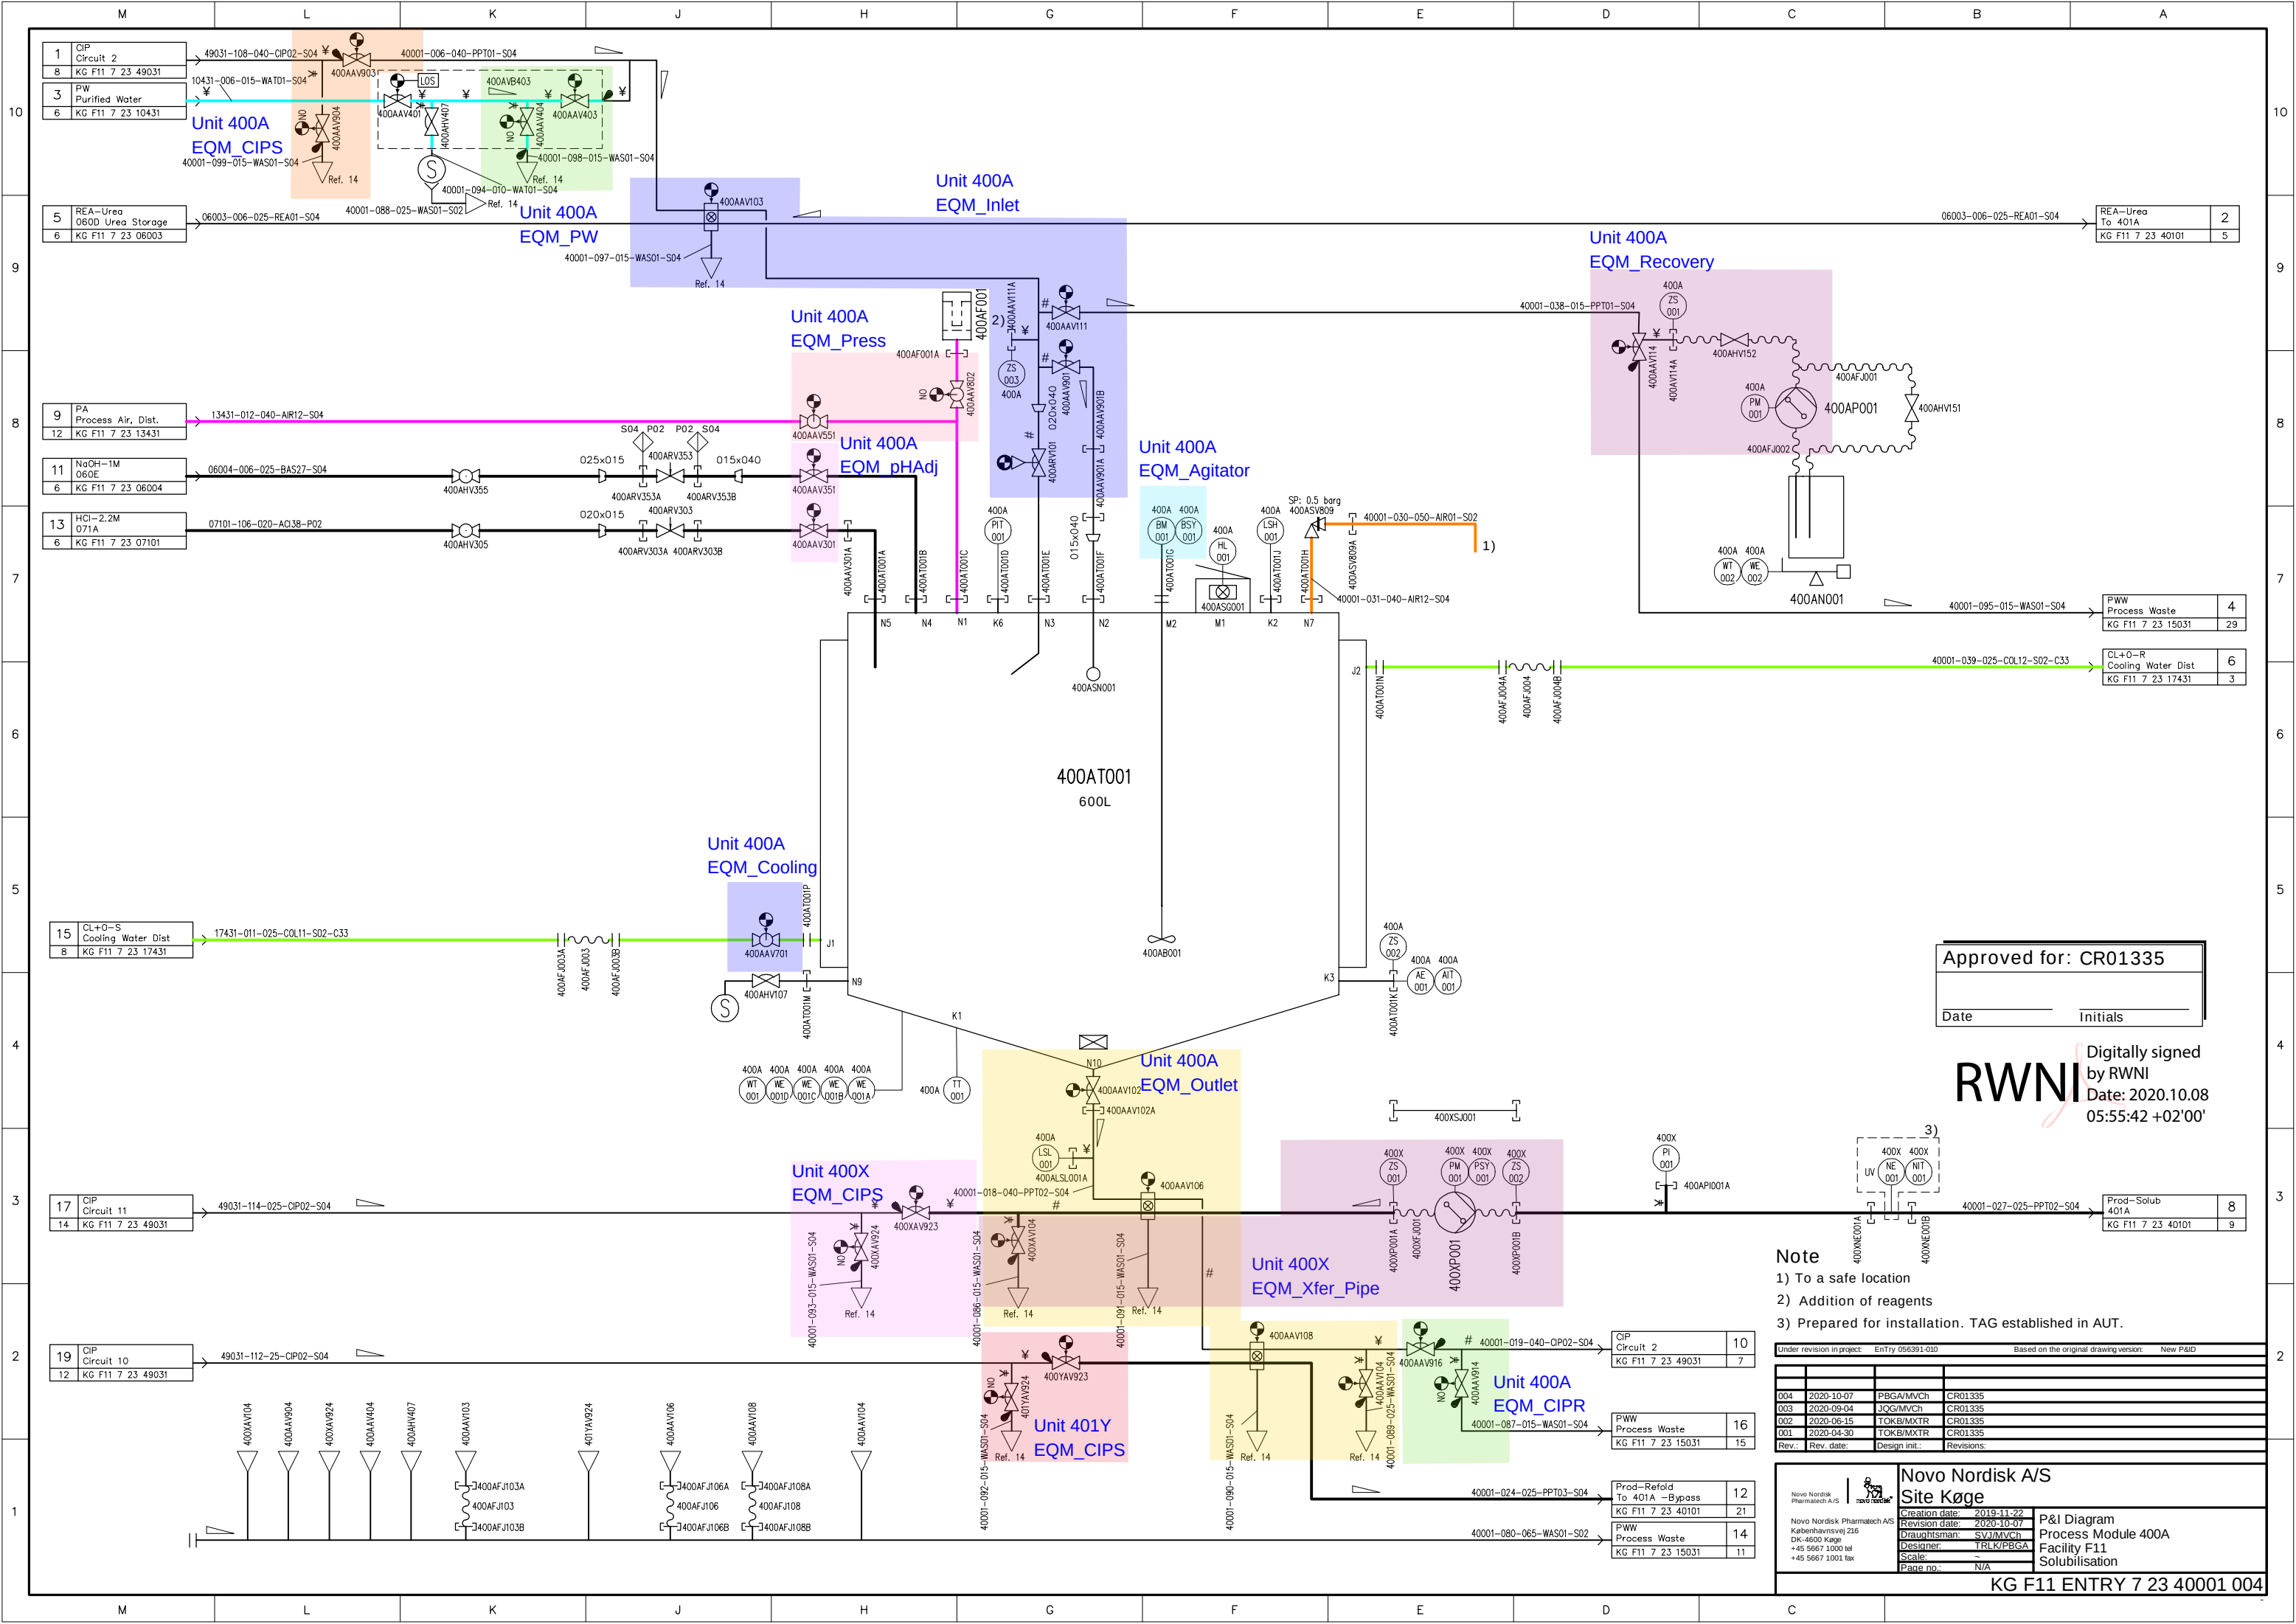

Approved for: CR01335

Date _____ Initials _____

RWNI Digitally signed by RWNI
Date: 2020.10.08 05:55:42 +02'00'

- Note**
- 1) To a safe location
 - 2) Addition of reagents
 - 3) Prepared for installation. TAG established in AUT.

Under revision in project: EnTry 056391-010		Based on the original drawing version: New P&ID	
004	2020-10-07	PBGA/MVCh	CR01335
003	2020-09-04	JQGM/MVCh	CR01335
002	2020-06-15	TOKB/MXTR	CR01335
001	2020-04-30	TOKB/MXTR	CR01335
Rev.:	Rev. date:	Design init.:	Revisions:
Novo Nordisk A/S Site Køge			
Novo Nordisk Pharmatech A/S Københavnvej 216 DK-4600 Køge +45 5667 1000 tel +45 5667 1001 fax		Creation date: 2019-11-22 Revision date: 2020-10-07 Draughtsman: SVJ/MVCh Designer: TRK/PBGA Scale: ~ Page no.: N/A	
P&I Diagram Process Module 400A Facility F11 Solubilisation		KG F11 ENTRY 7 23 40001 004	